



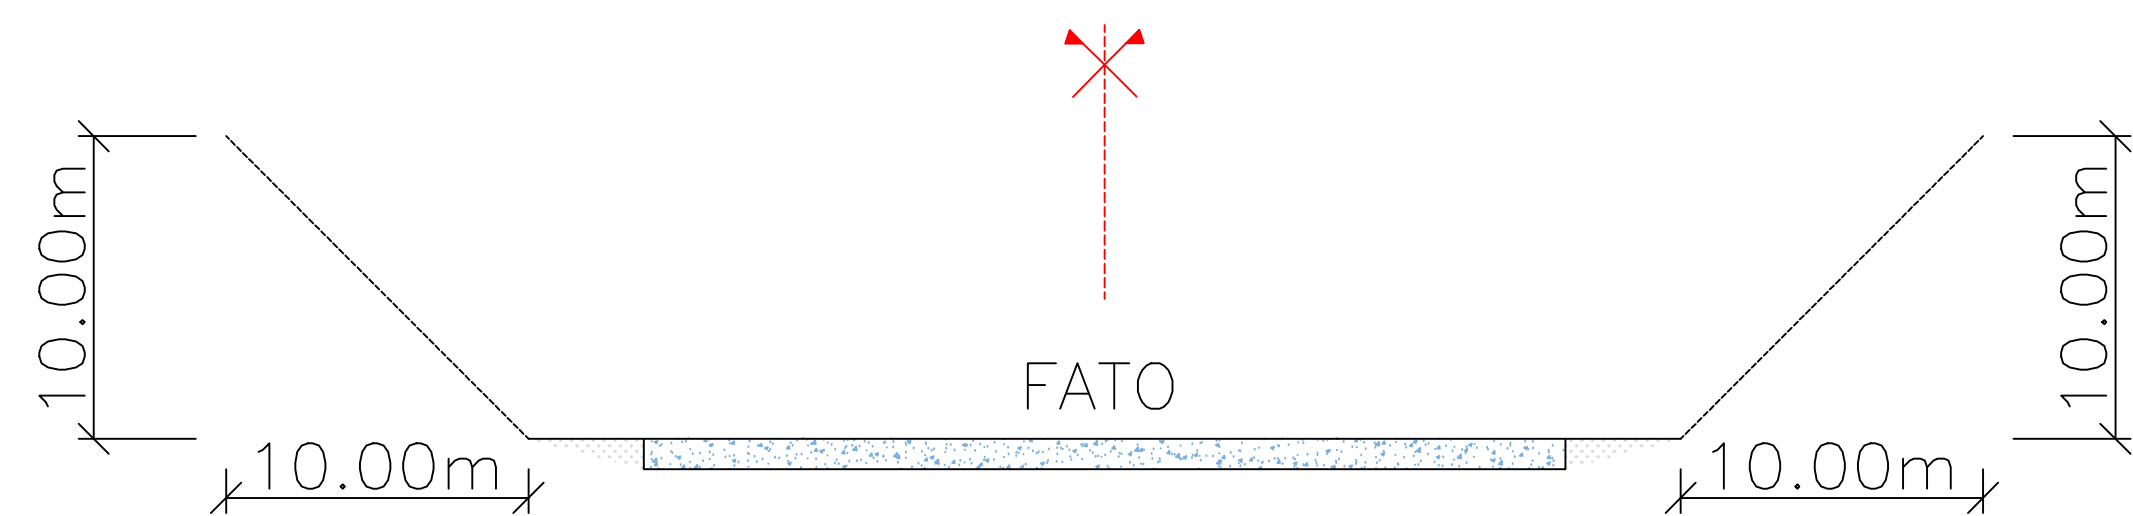


PISTA E ROTA DE TÁXI TERRESTRE E AÉREO – PLANTA
ESCALA 1:125

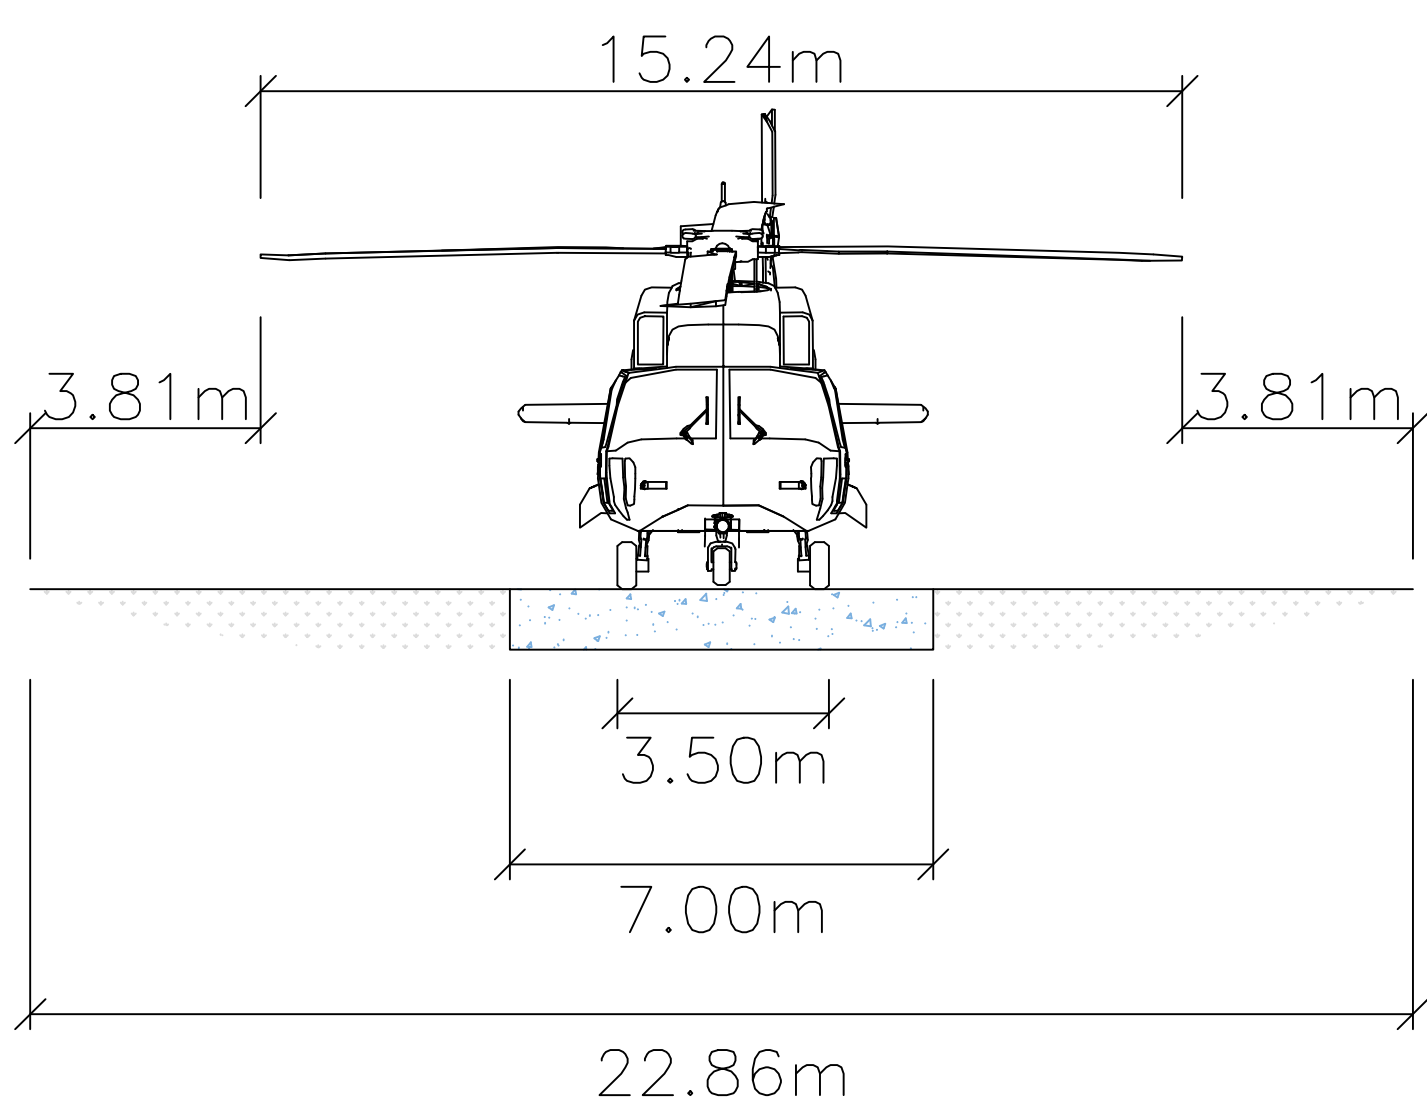


RAMPA LATERAL PROTEGIDA – CORTE AA
ESCALA 1:250

Elemento	Fórmula adotada	Valor adotado
Aeronave crítica	BETA ALIA VTOL	D = 15,24 m
UCW adotado	Hipótese conservadora	3,50 m
TLOF	$1,00 \times D$	15,24 m
FATO	$2,00 \times D$	30,48 m
Área de segurança	$2,50 \times D$	38,10 m
Faixa além do FATO	$(38,10 - 30,48)/2$	3,81 m por lado
Taxiway pavimentada	$2 \times UCW$	7,00 m
Rota de táxi terrestre	$1,50 \times D$	22,86 m
Faixa além da taxiway	$(22,86 - 7,00)/2$	7,93 m por lado
Rota de táxi aéreo	$2,00 \times D$	30,48 m
Faixa além da taxiway para air taxi	$(30,48 - 7,00)/2$	11,74 m por lado

PISTA E ROTA DE TÁXI TERRESTRE – VISTA
ESCALA 1:125

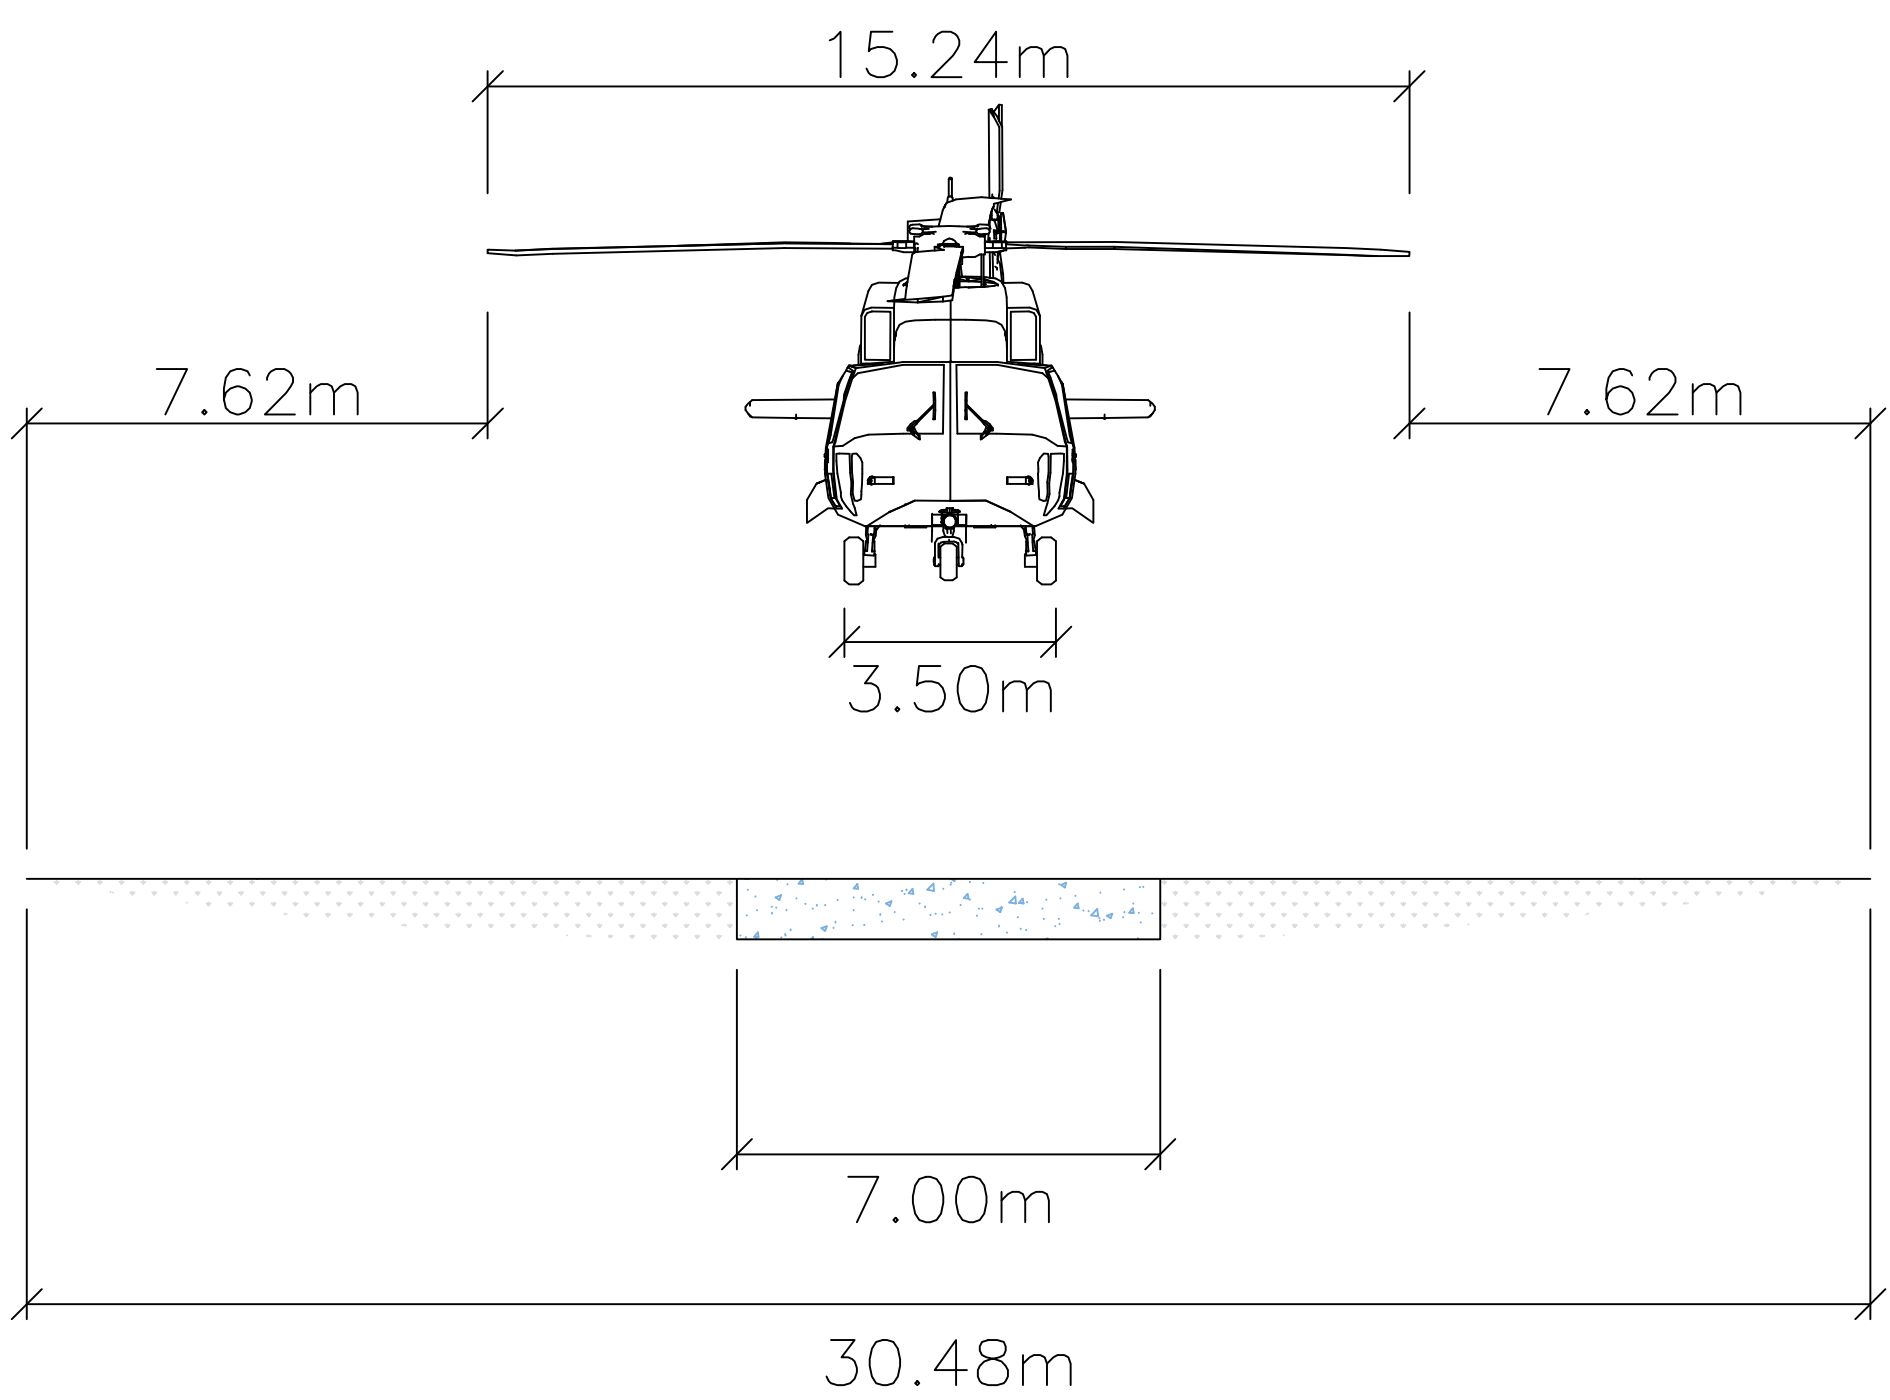

PISTA E ROTA DE TÁXI AÉREO – VISTA
ESCALA 1:125

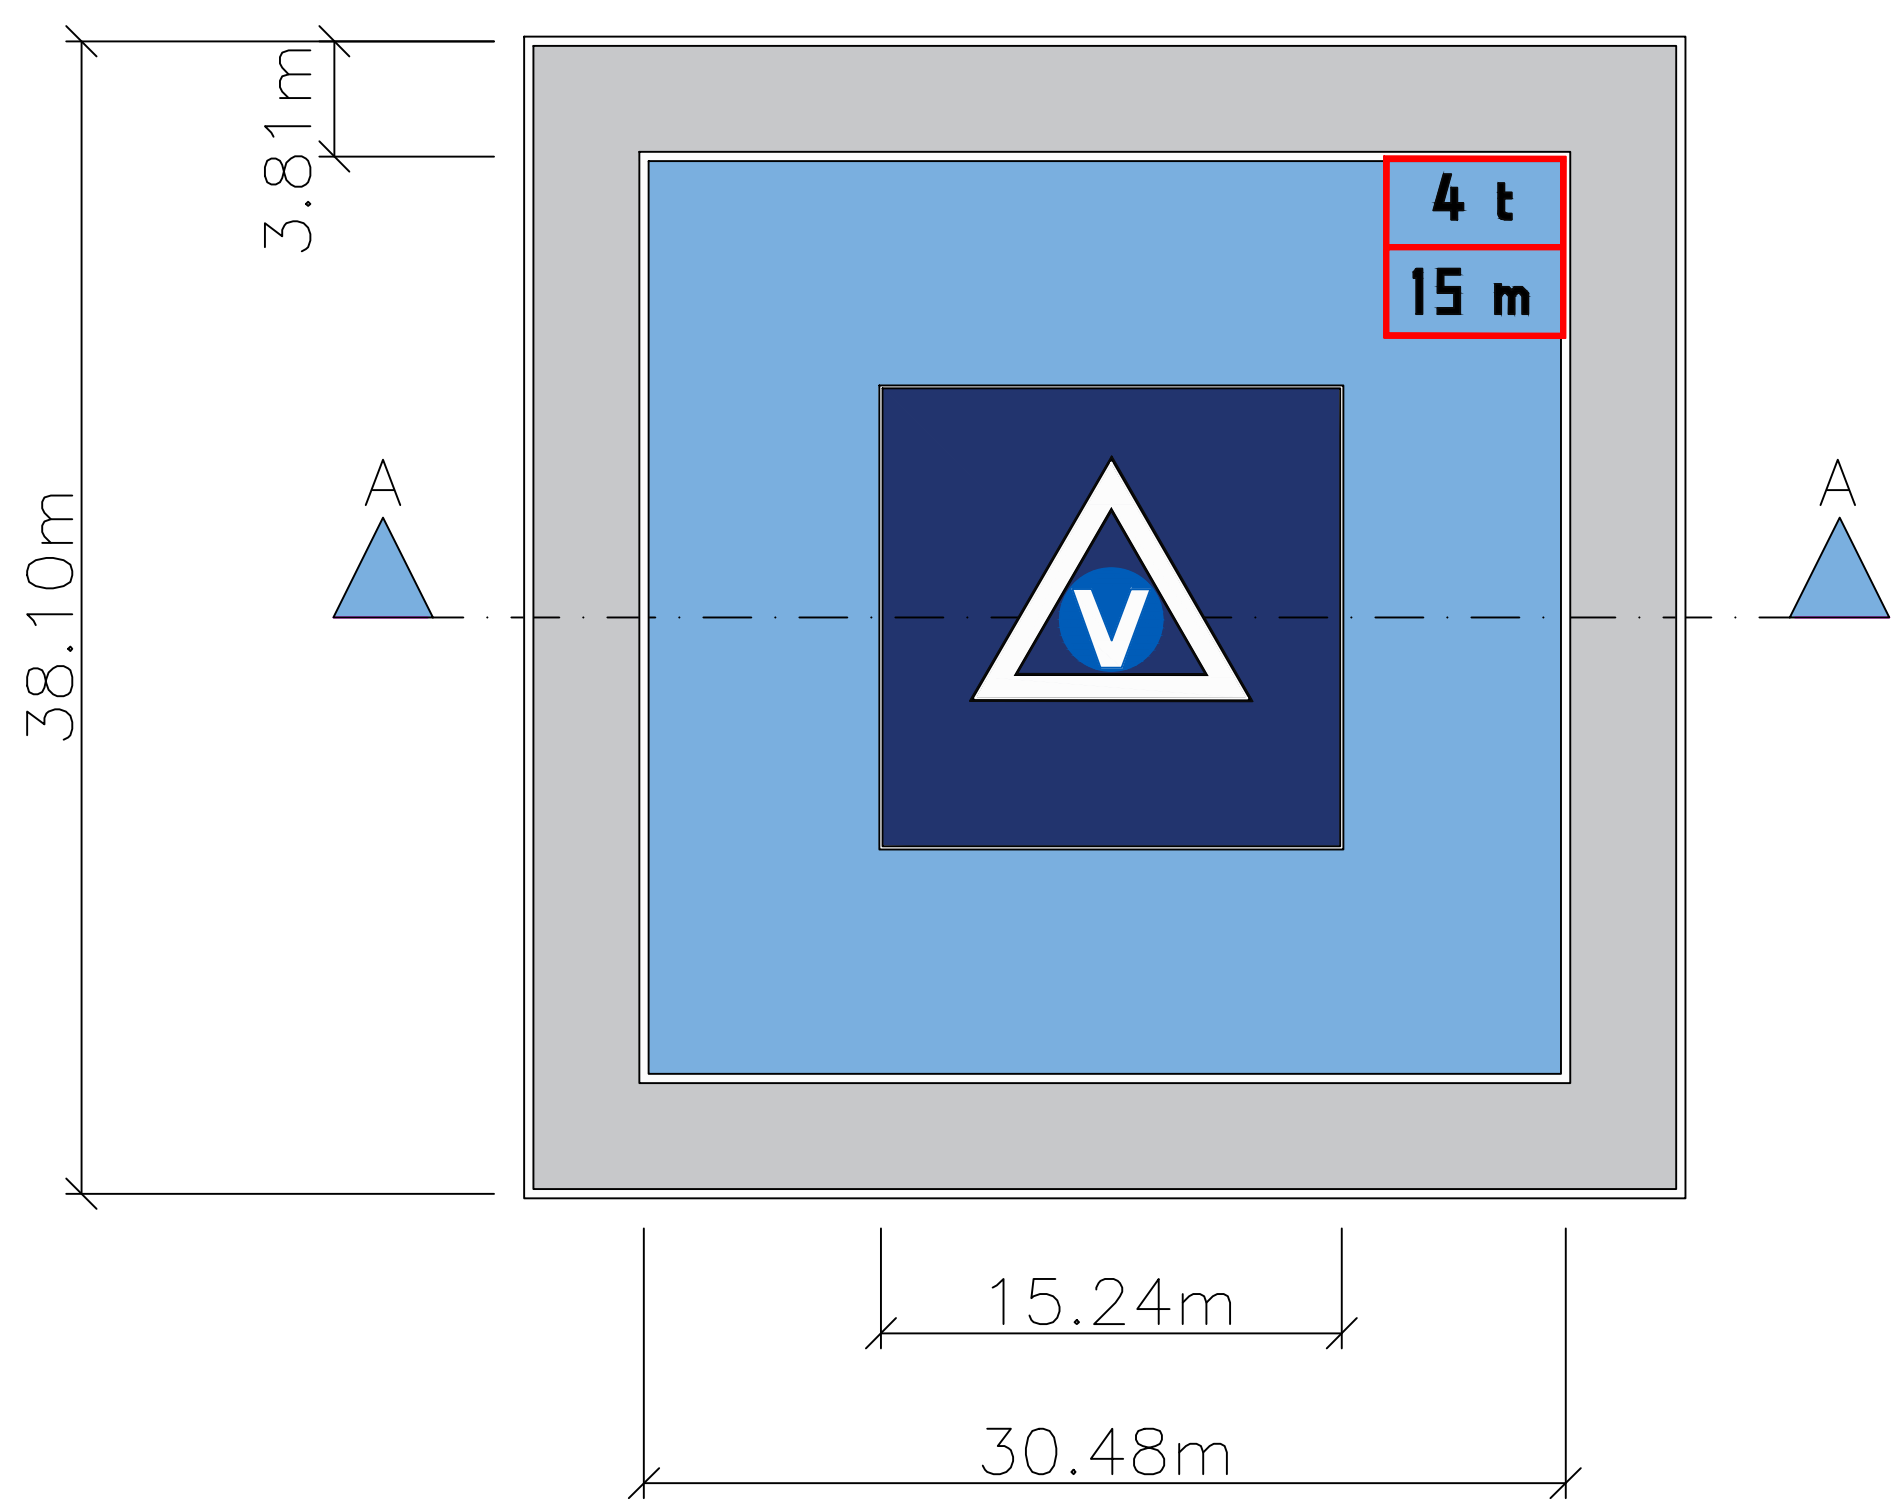

FATO E ÁREA DE SEGURANÇA ASSOCIADA – PLANTA
ESCALA 1:250



ESQUEMA DO TRECHO

PROJETO PRÉ-DIMENSIONAMENTO VERTIPORTO

01/01

INSTITUTO TECNOLÓGICO DE AERONÁUTICA IT-214 - MOBILIDADE AÉREA URBANA
Discentes: Caio Honorato Antonio, Eduardo de Vasconcellos, Gianluca Furtado, Rafael Almeida
Docente: Prof. Dr. Marcelo Xavier Guterres

