

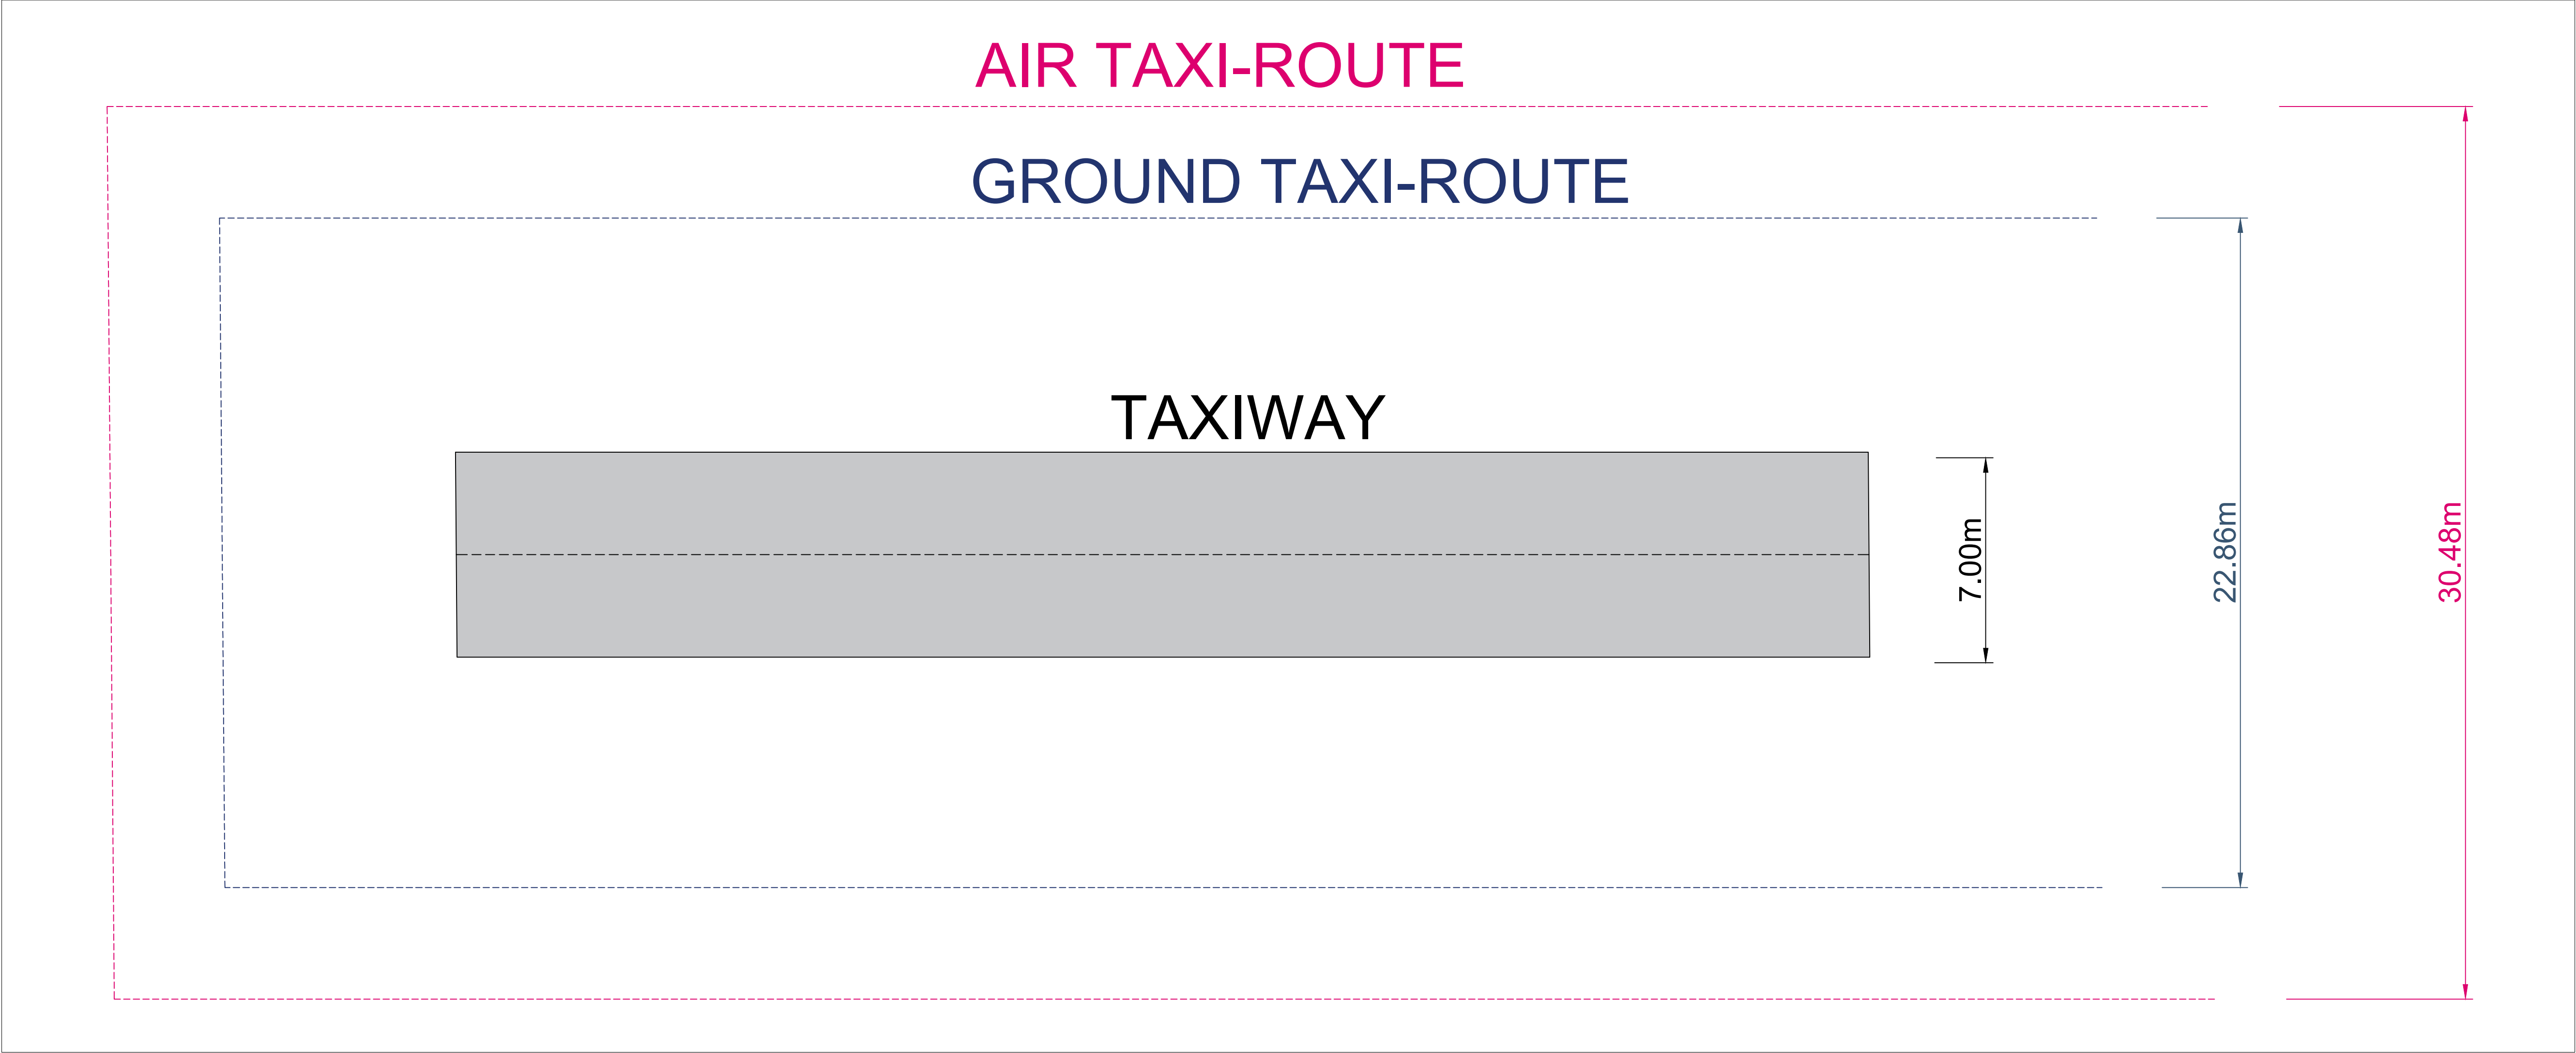


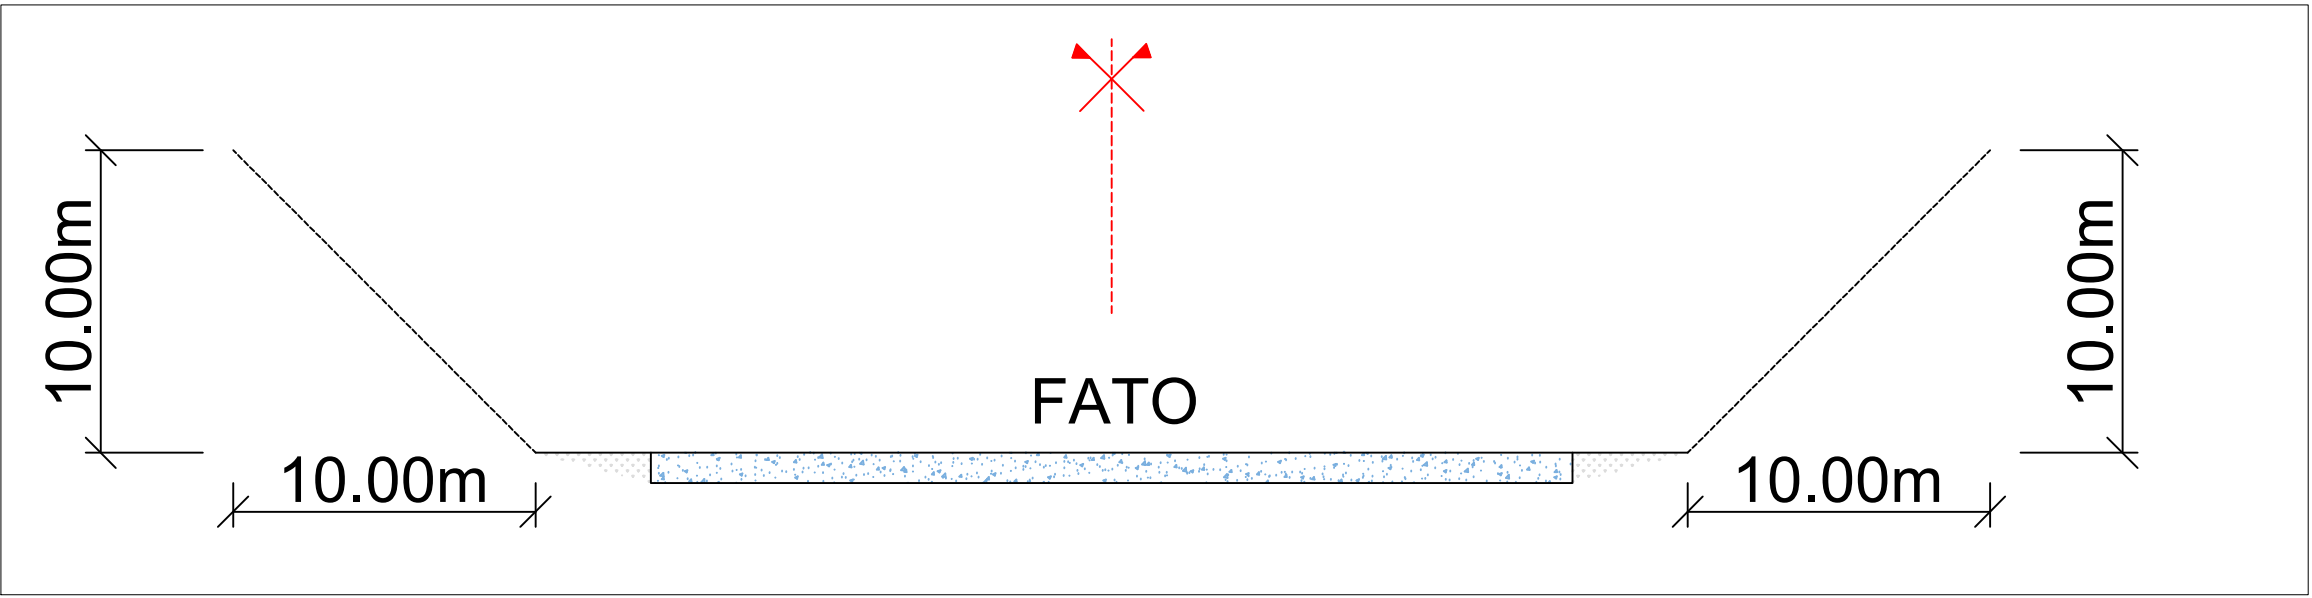


PISTA E ROTA DE TÁXI TERRESTRE E AÉREO - PLANTA

ESCALA 1:125

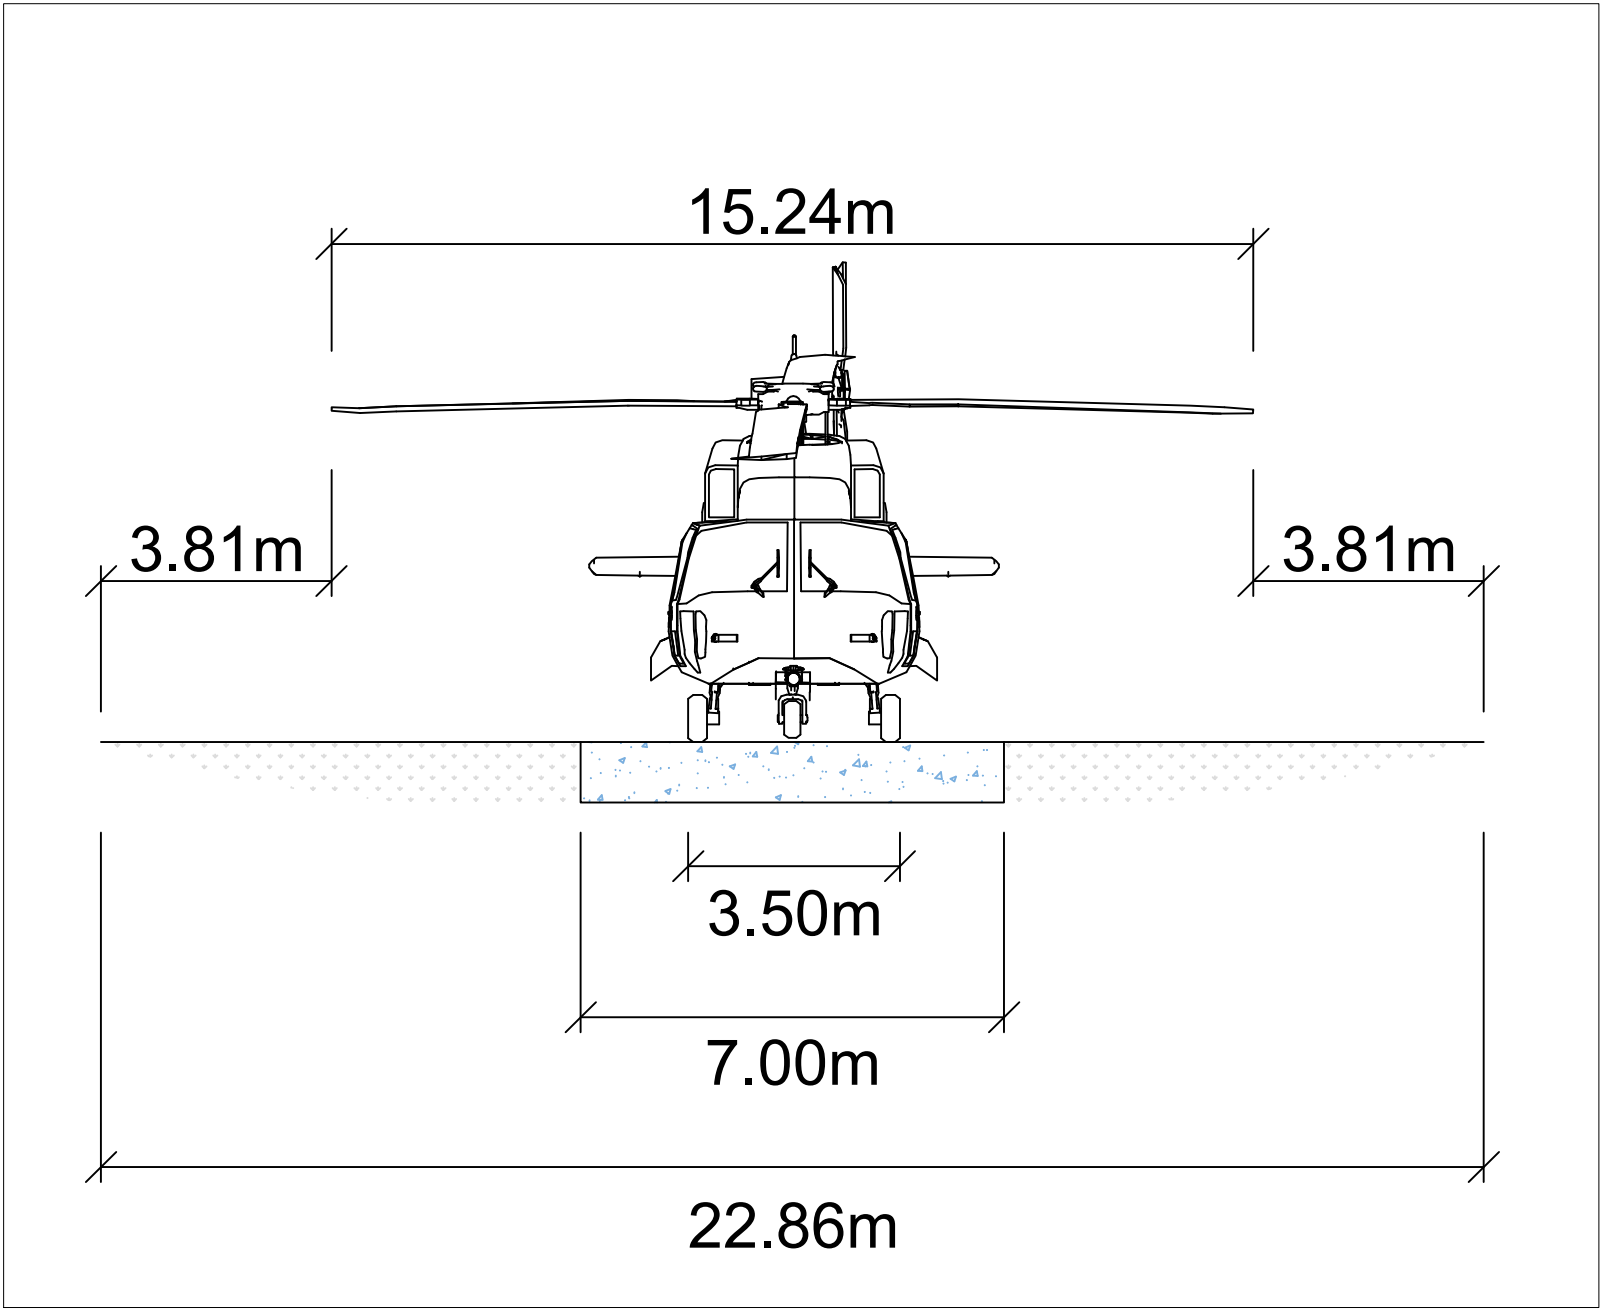

RAMPA LATERAL PROTEGIDA - CORTE AA

ESCALA 1:250

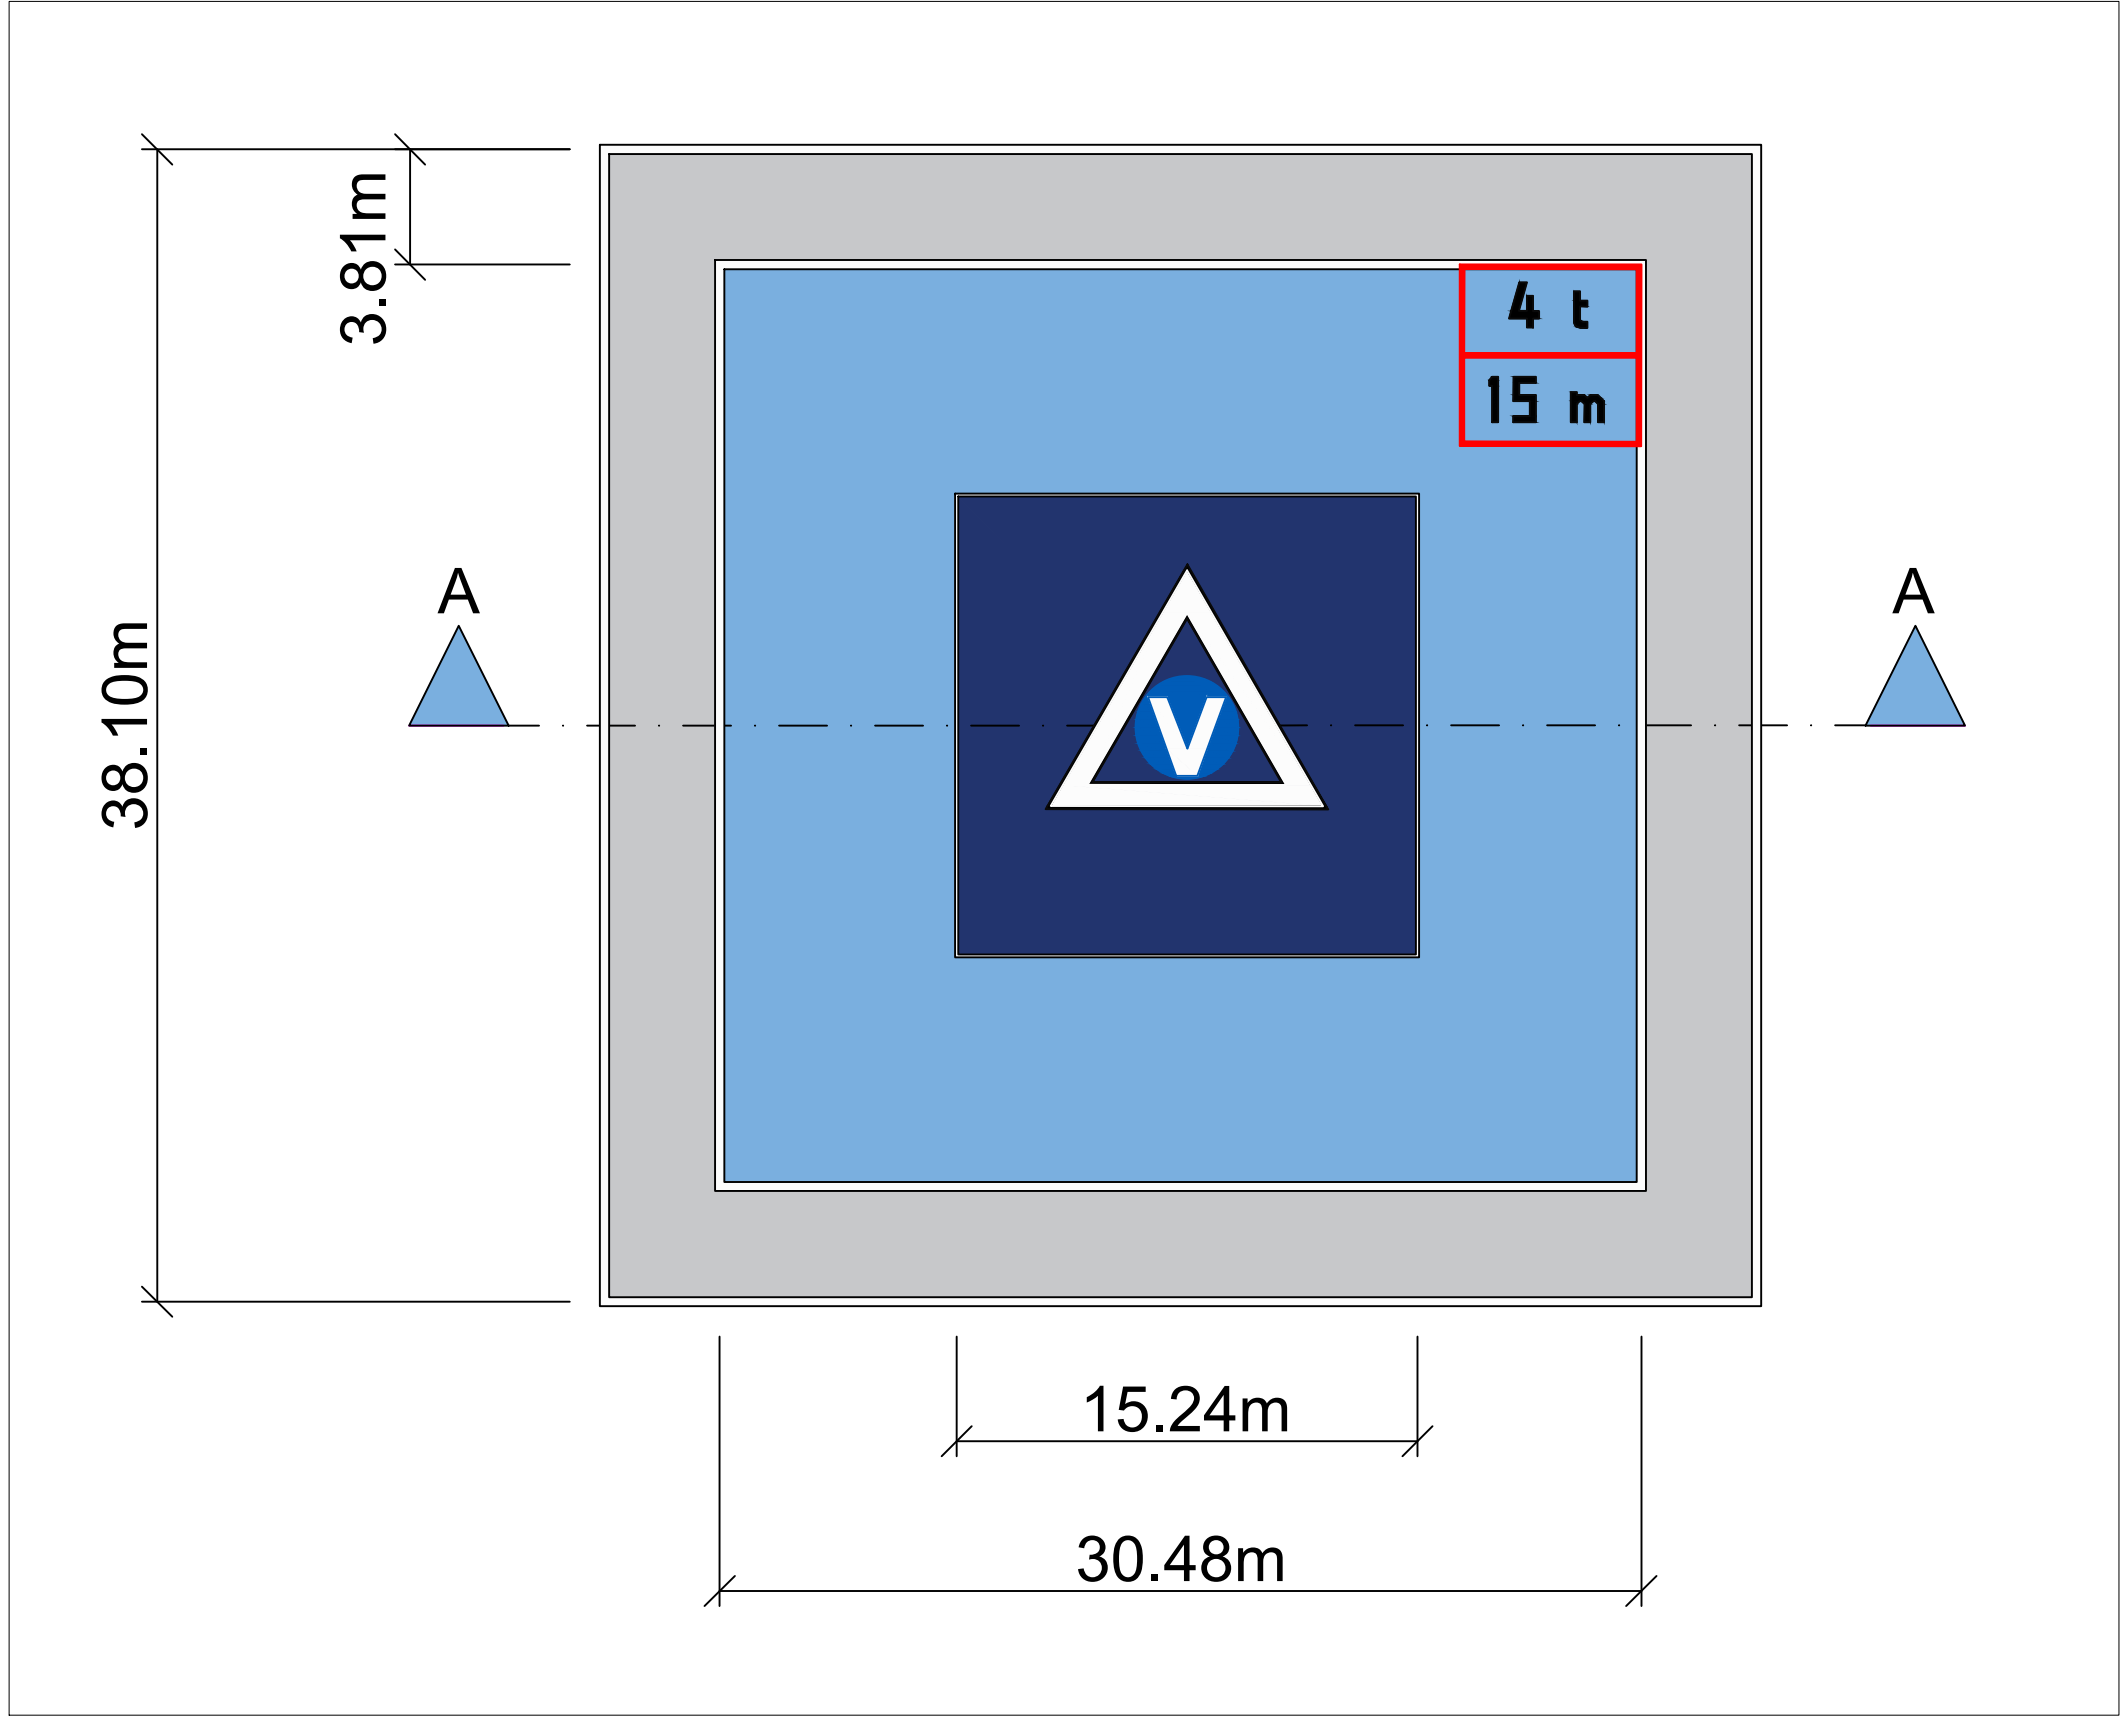

FATO E ÁREA DE SEGURANÇA ASSOCIADA - PLANTA

ESCALA 1:250


Elemento	Fórmula adotada	Valor adotado
Aeronave crítica	BETA ALIA VTOL	D = 15,24 m
UCW adotado	Hipótese conservadora	3,50 m
TLOF	$1,00 \times D$	15,24 m
FATO	$2,00 \times D$	30,48 m
Área de segurança	$2,50 \times D$	38,10 m
Faixa além do FATO	$(38,10 - 30,48)/2$	3,81 m por lado
Taxiway pavimentada	$2 \times UCW$	7,00 m
Rota de táxi terrestre	$1,50 \times D$	22,86 m
Faixa além da taxiway	$(22,86 - 7,00)/2$	7,93 m por lado
Rota de táxi aéreo	$2,00 \times D$	30,48 m
Faixa além da taxiway para air taxi	$(30,48 - 7,00)/2$	11,74 m por lado

LEGENDA

- TLOF
- FATO
- ÁREA DE SEGURANÇA
- TAXIWAY PAVIMENTADA
- GROUND TAXI-ROUTE
- AIR TAXI-ROUTE
- AERONAVE CRÍTICA
- EIXO TAXIWAY

PISTA E ROTA DE TÁXI TERRESTRE - VISTA

ESCALA 1:125

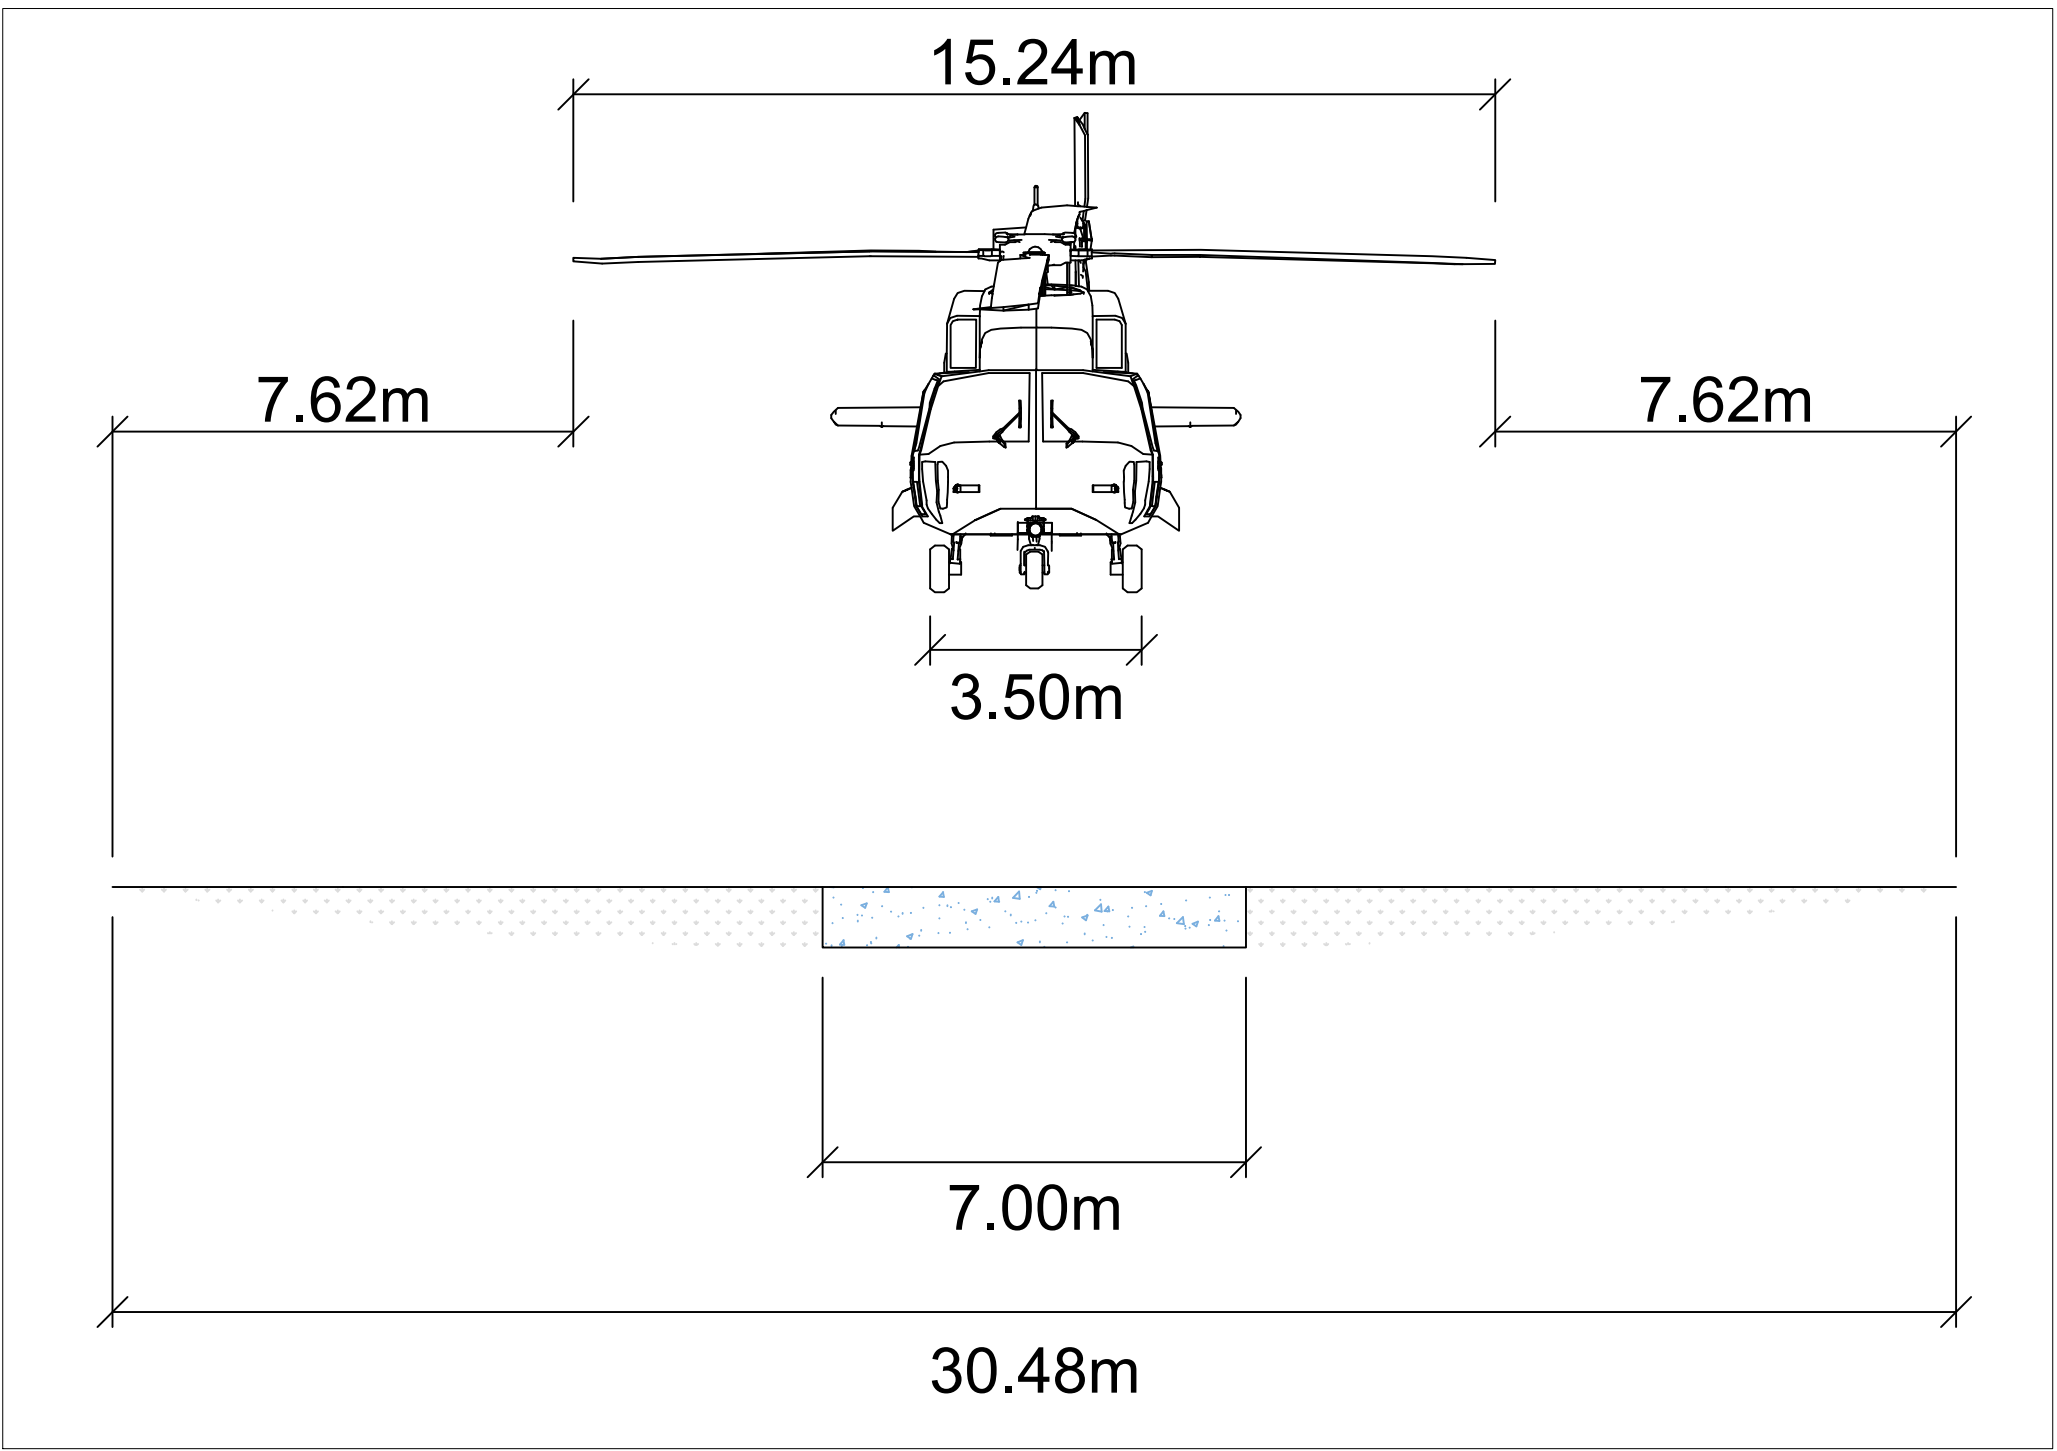

PISTA E ROTA DE TÁXI AÉREO - VISTA

ESCALA 1:125



ESQUEMA DO TRECHO

		INSTITUTO TECNOLÓGICO DE AERONÁUTICA - ITA IT-214 MOBILIDADE AÉREA URBANA		PRANCHA 03/0X	
		FOLHA 03 - DIMENSIONAMENTO LADO AR		FASE: ESTUDO PRELIMINAR	
AUTORES Caio Honorato Antonio Eduardo de Vasconcelos Giancarlo Furtado Rafael Almeida		DOCENTE Prof. Dr. Marcelo Xavier Guterres		LOCAL Rodoviária do Plano Piloto Brasília - DF	
SISTEMA DE COORDENADAS SIRGAS 2000 / UTM 23S EPSG 31983		DATA 30/06/2026		REV 0	
REV	DATA	DESCRIÇÃO			RESP.
0	30/06/2026	EMIÇÃO INICIAL - ESTUDO PRELIMINAR			AUTORES

