



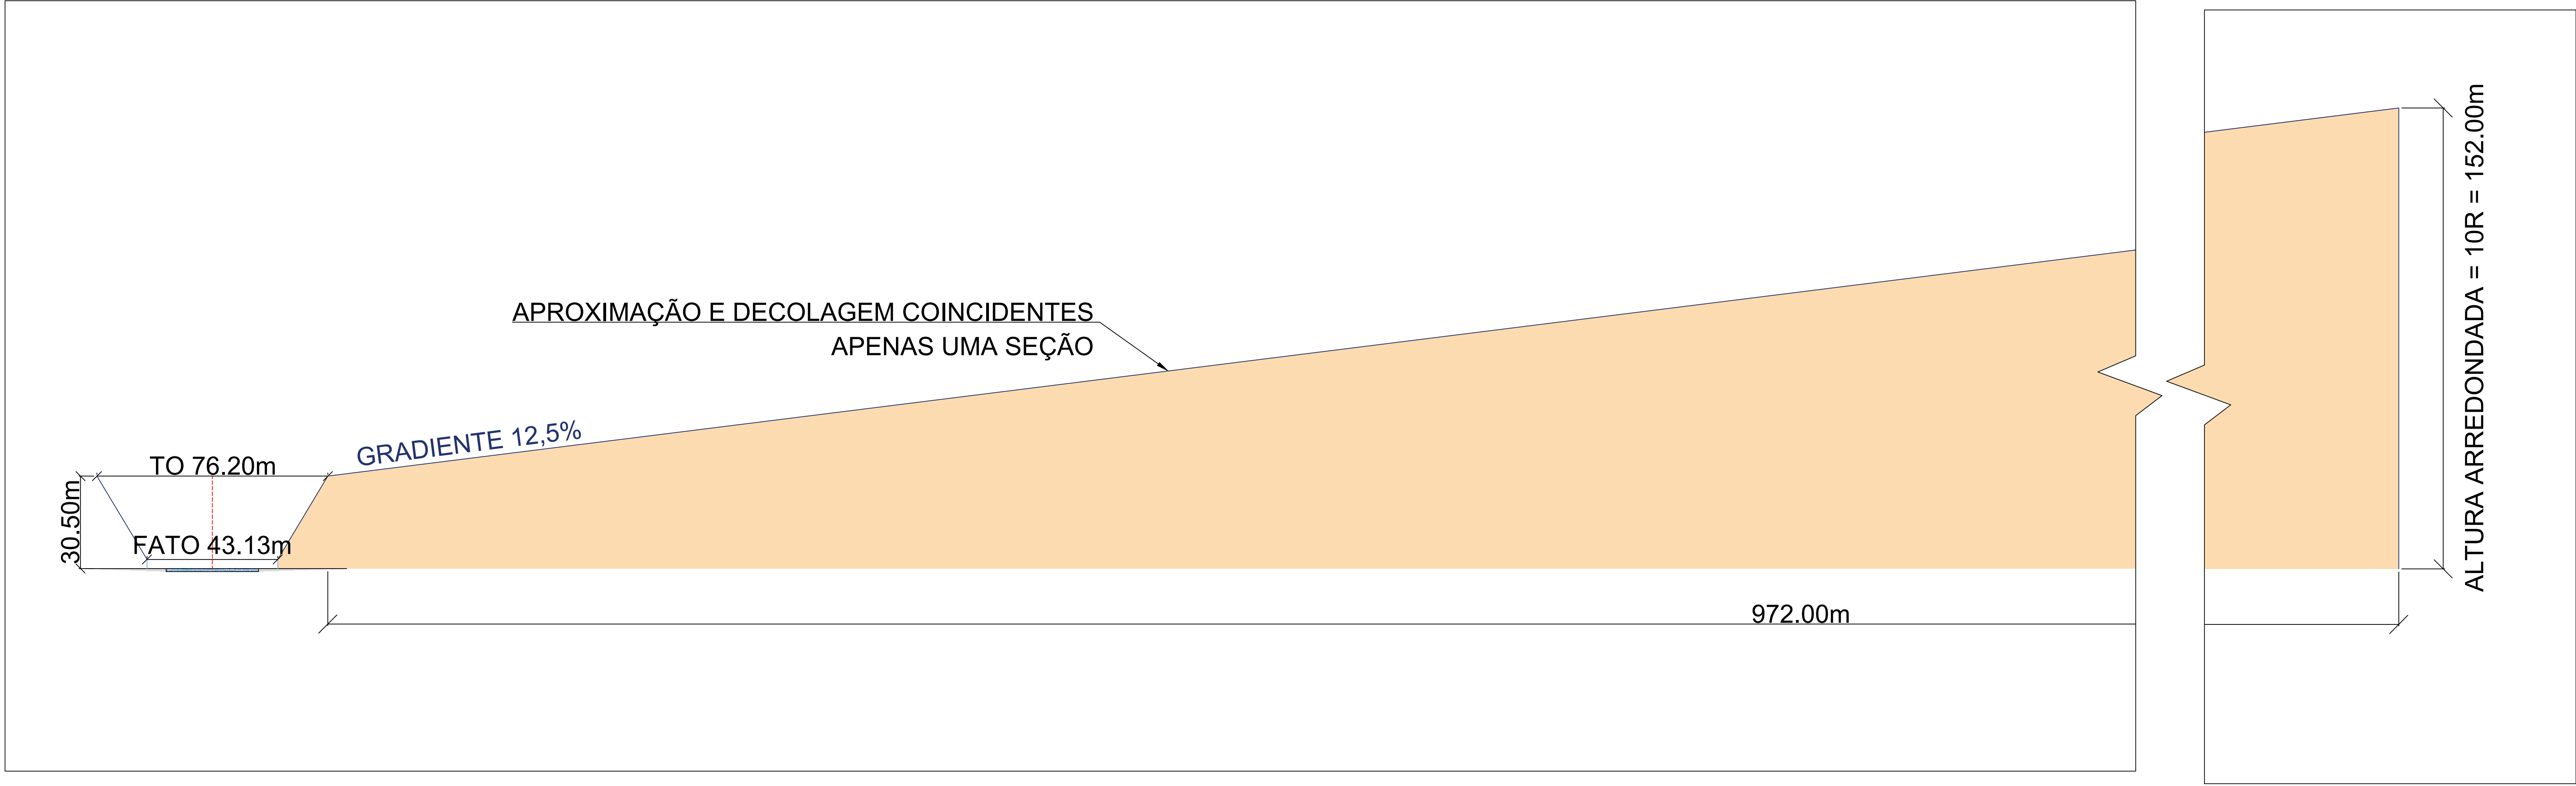

SUPERFÍCIE DE PROTEÇÃO EASA UMA DIREÇÃO - CORTE AA

ESCALA 1:1000

Elemento	Fórmula adotada	Valor adotado
h1	EASA	3,00 m
h2	EASA	30,50 m
Altura final OLS	EASA	152,0 m
Gradiente	EASA	12,5% = 1V:8H
øFATO	$2,83 \times D$	43,13 m
øTO	$5,00 \times D$	76,20 m
Desnível h2 até topo	$152 - 30,50$	121,50 m
Projeção horizontal	$121,50 / 0,125$	972,0 m
Distância centro-final	$38,10 + 972,00$	1.010,10 m

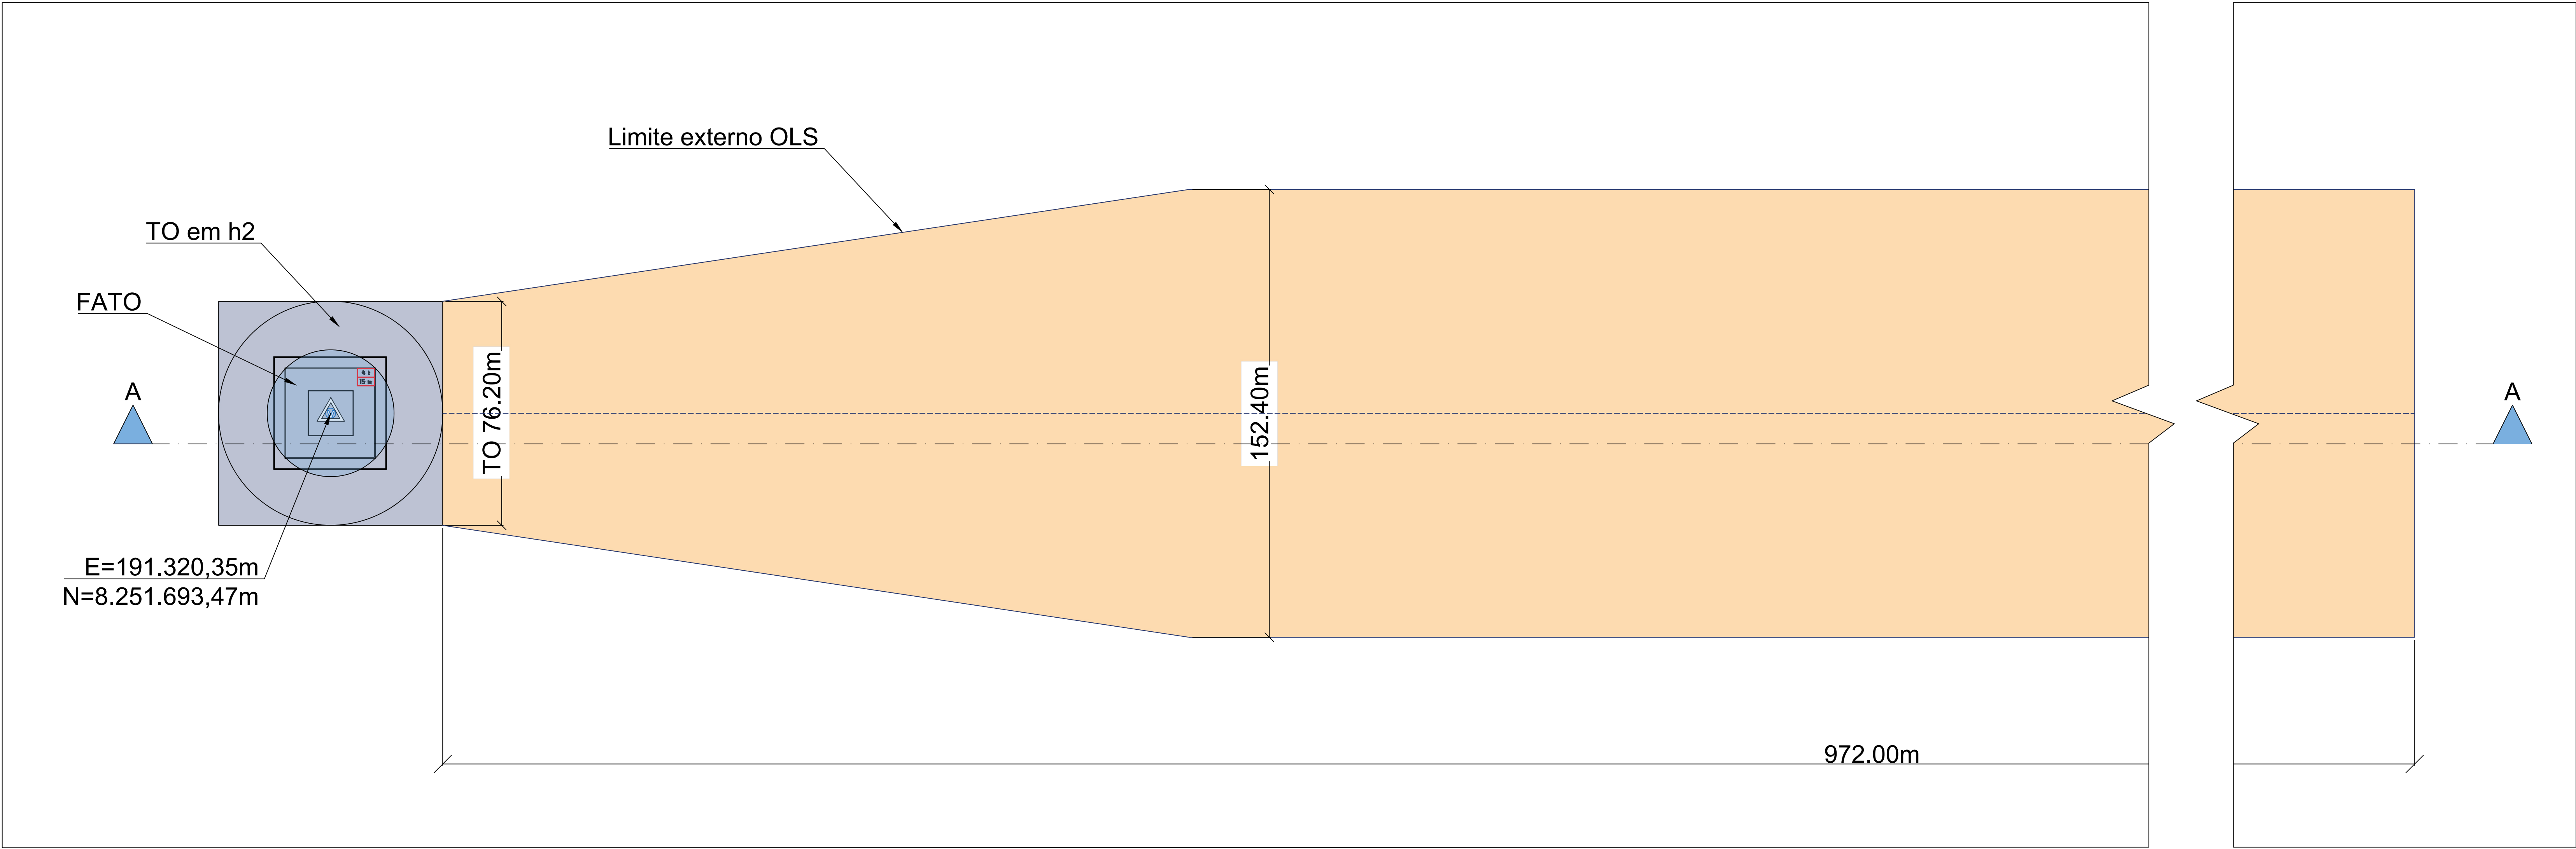

SUPERFÍCIE DE PROTEÇÃO EASA UMA DIREÇÃO - PLANTA

ESCALA 1:1000

LEGENDA

FATO / Área central de referência

TO em h2 / Volume inicial


Superfície livre de obstáculos - OLS

Limite da superfície de proteção

Eixo de aproximação/decolagem



ESQUEMA DO TRECHO

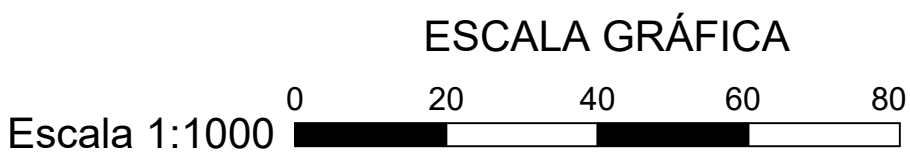

		INSTITUTO TECNOLÓGICO DE AERONÁUTICA - ITA IT-214 MOBILIDADE AÉREA URBANA		PRANCHA 04/0X	
		ANTEPROJETO DE VERTIPOSTO - RODOVIÁRIA DO PLANO PILOTO		FASE: ESTUDO PRELIMINAR	
		FOLHA 04 - SUPERFÍCIE DE PROTEÇÃO - LADO AR			
AUTORES Caio Honorato Antonio Eduardo de Vasconcelos Giancarlo Furtado Rafael Almeida		DOCENTE Prof. Dr. Marcelo Xavier Guterres		LOCAL Rodoviária do Plano Piloto Brasília - DF	
SISTEMA DE COORDENADAS SIRGAS 2000 / UTM 23S EPSG 31983		DATA 30/06/2026		REV 0	
REV	DATA	DESCRIÇÃO			RESP.
0	30/06/2026	EMIÇÃO INICIAL - ESTUDO PRELIMINAR			AUTORES